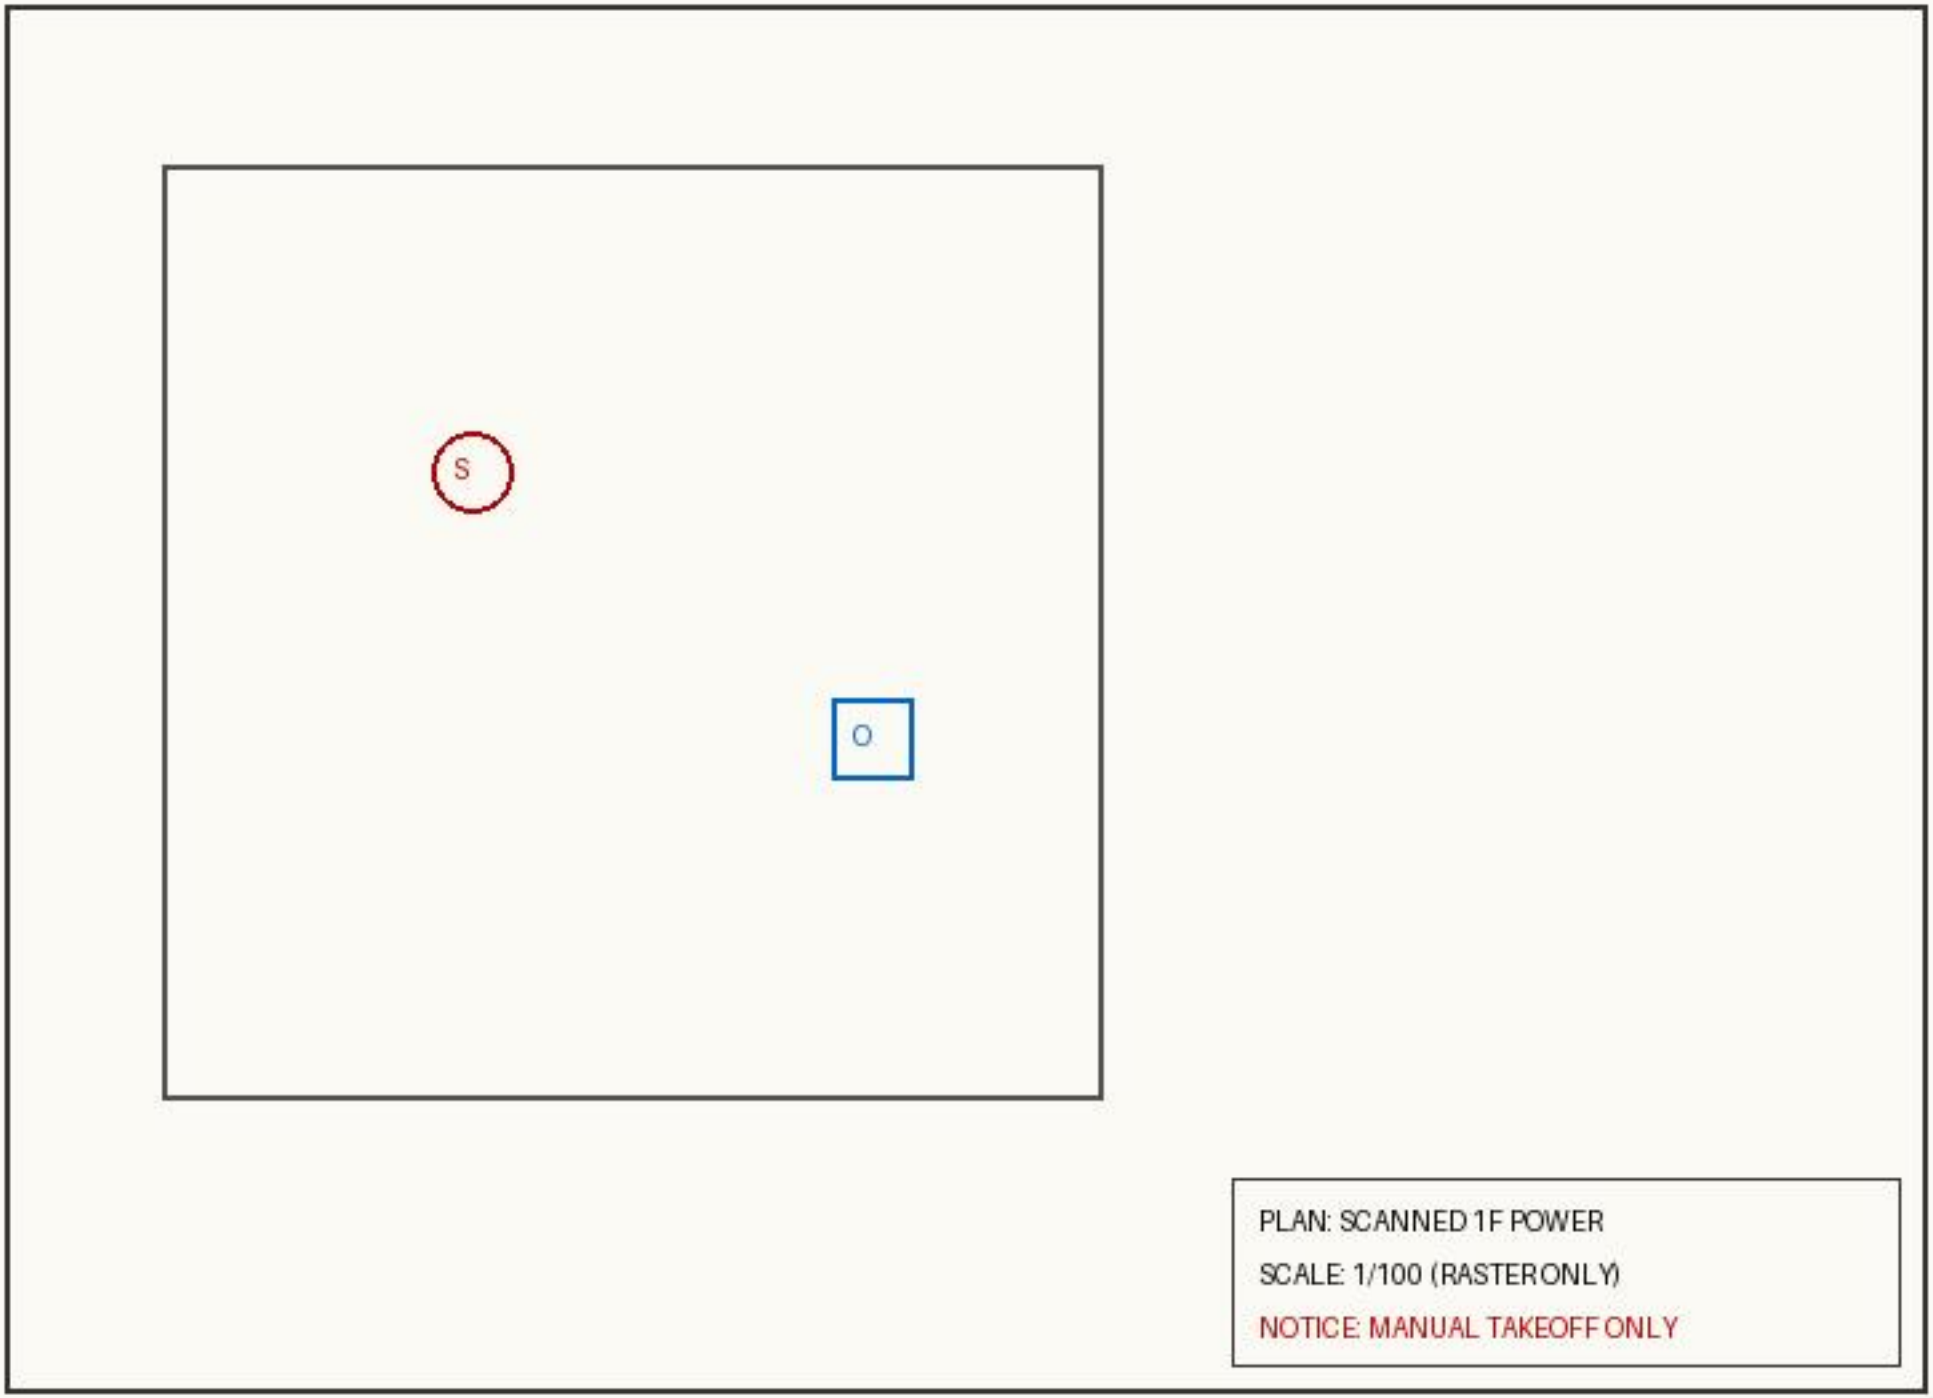

PLAN: SCANNED 1F POWER

SCALE: 1/100 (RASTER ONLY)
 
NOTICE: MANUAL TAKEOFF ONLY